


TO ENSURE ADEQUATE CONSTRUCTION MONITORING IS CARRIED OUT, PLEASE CALL BVT OPERATIONS ON +64 3 371 7593 AT LEAST FIVE BUSINESS DAYS PRIOR TO PROJECT CONSTRUCTION COMMENCEMENT.

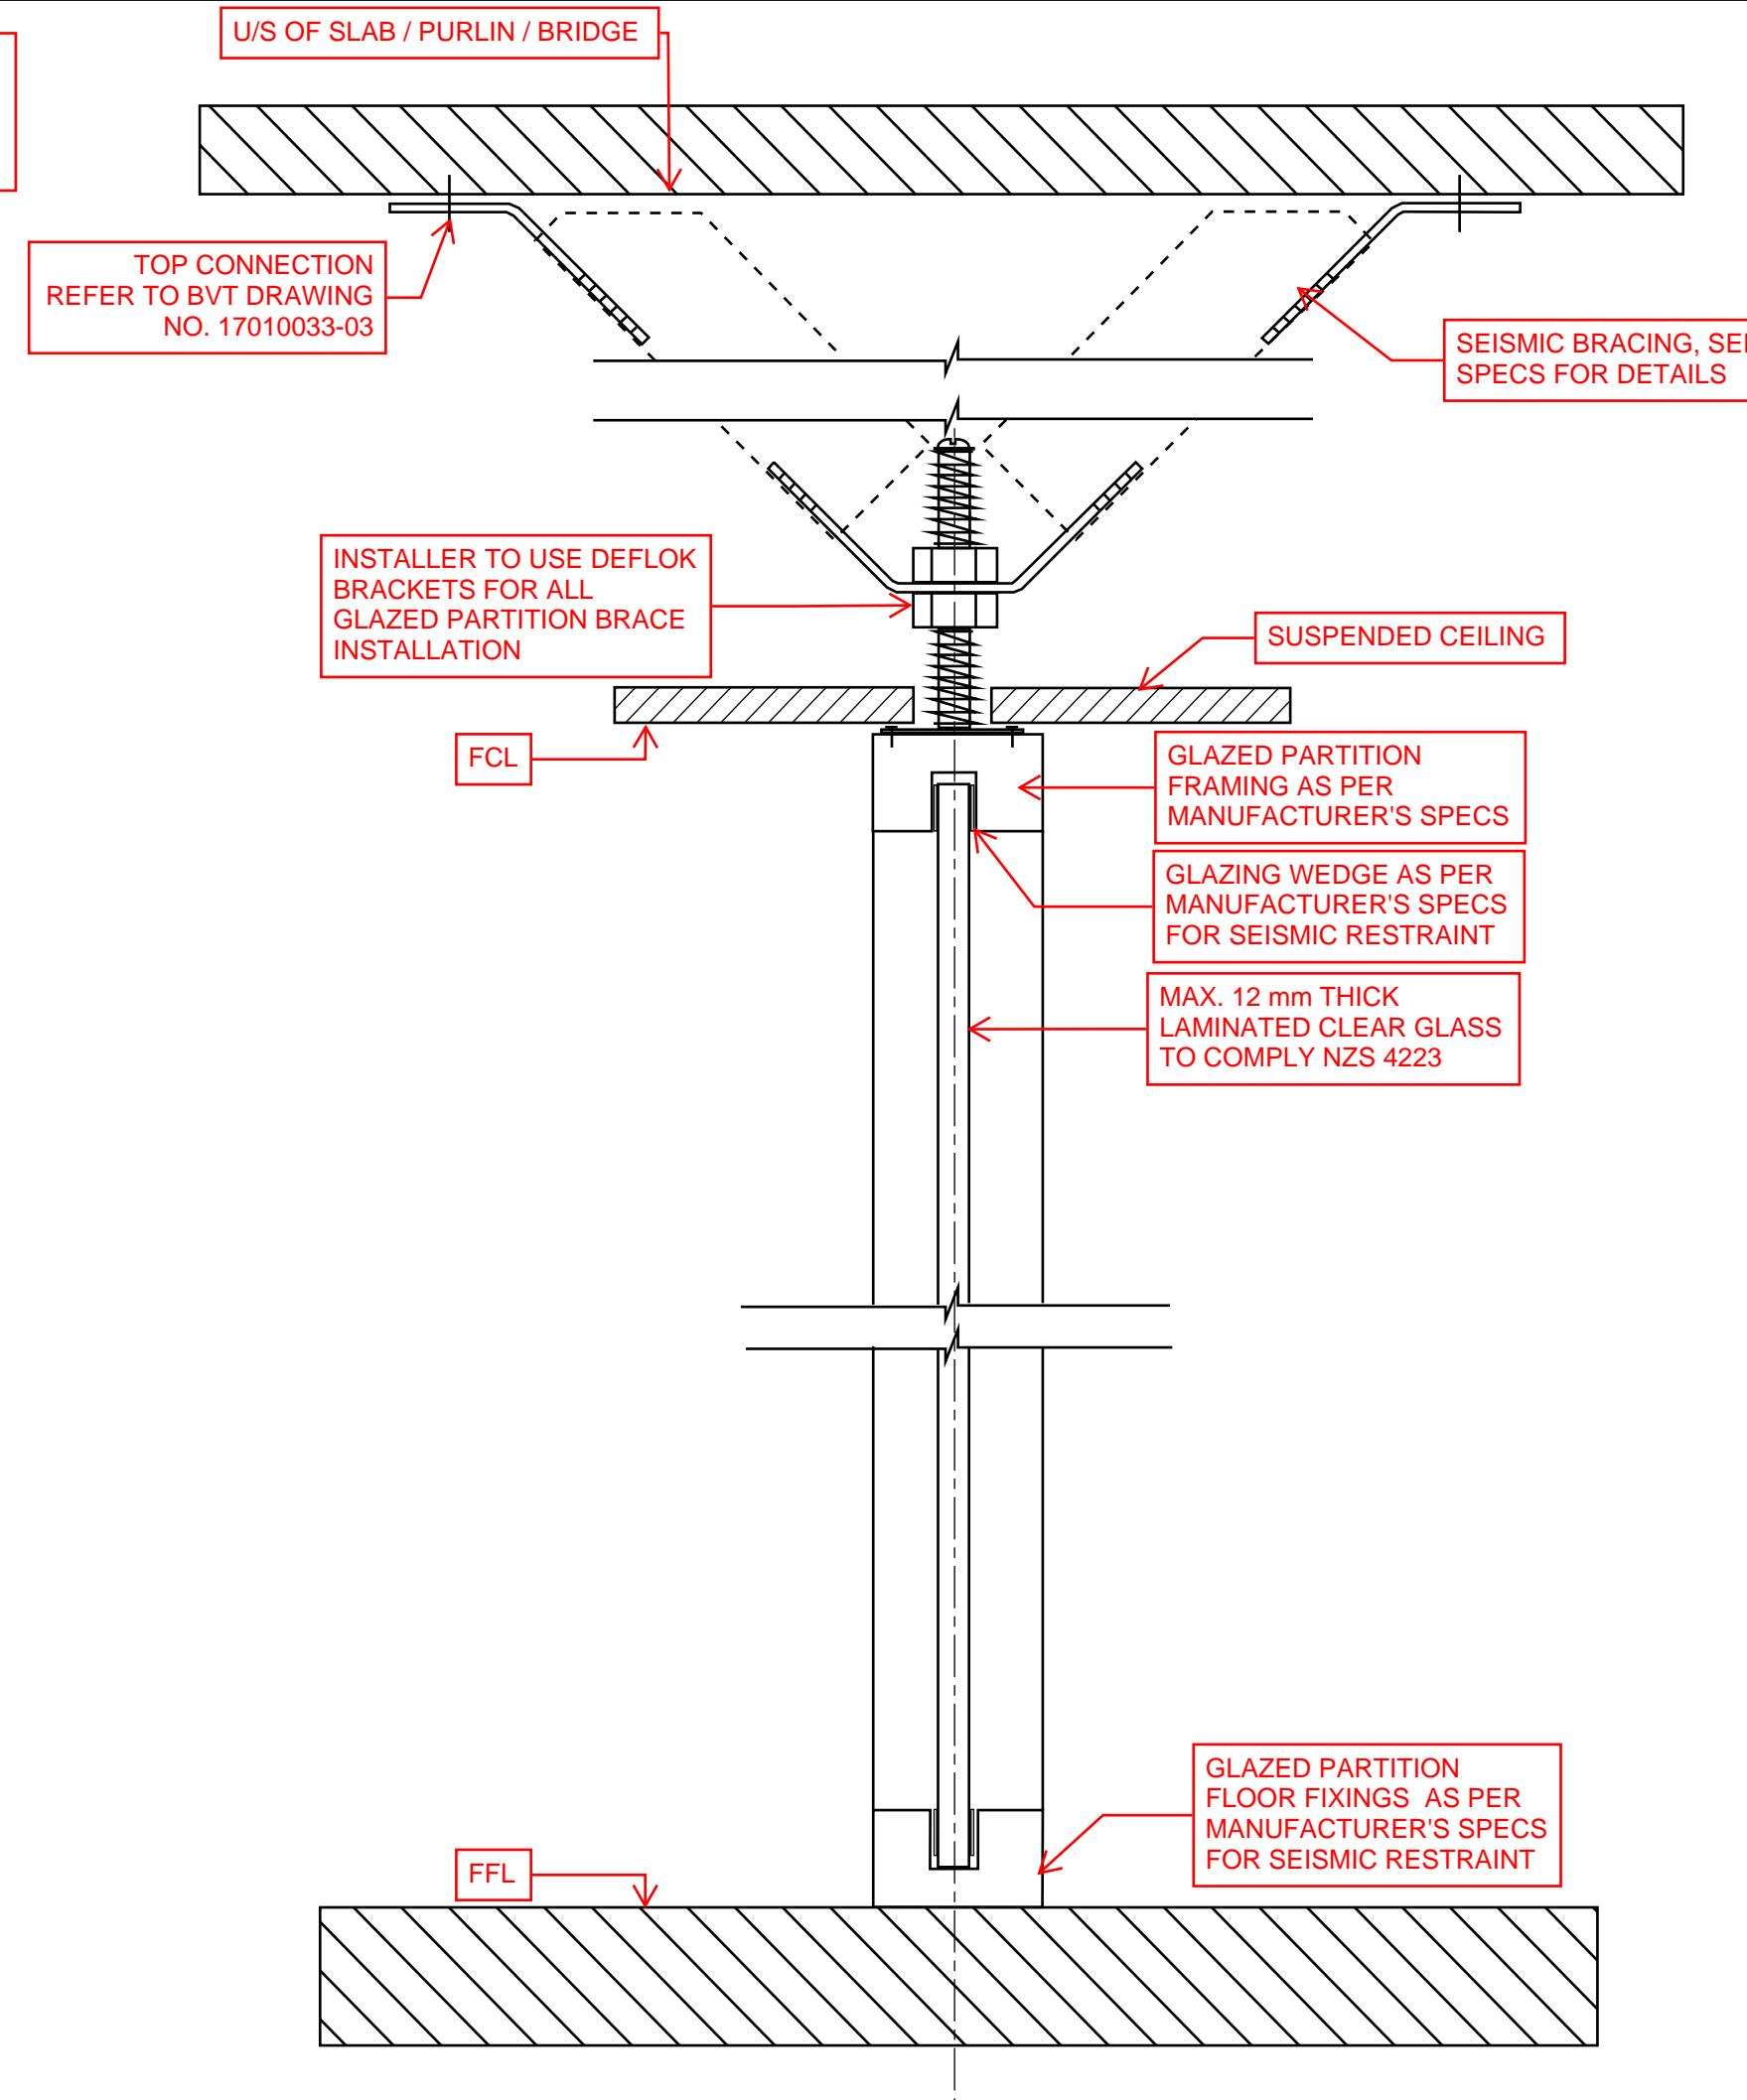

- NOTES:
1. REFER SPECIFICATION SHEET FOR CONTRACTOR AND INSTALLATION REQUIREMENTS
  2. ANY CHANGES ON SITE TO BE APPROVED BY BVT
  3. BRACE SPACING FOR ALLOY HEAD TRACK TO BE MAX. 1200mm
  4. INSTALLER TO USE DEFLOK BRACKETS FOR BRACE INSTALLATION

DESIGNER:

**Brevity**

Victoria Park Market,  
Unit 72B,  
210 Victoria Street West  
Auckland 1010

+64 9 216 7104  
[www.teambrevity.com](http://www.teambrevity.com)

Tolerances (unless specified)	1-100	<1000	>1000
± 2	± 10	± 70	

All dim.  
in mm

Rev	Description
A	FOR CONSENT

Designed	BREVITY LTD	16/01/23
Drawn	BREVITY LTD	16/01/23
Approved	BREVITY LTD	16/01/23

SEISMIC BRACING LAYOUT -  
PARTITION GLAZED WALL  
UP TO CEILING HEIGHT

Scale  
Do not Scale