


TO ENSURE ADEQUATE CONSTRUCTION MONITORING IS CARRIED OUT, PLEASE CALL BVT OPERATIONS ON +64 3 371 7593 AT LEAST FIVE BUSINESS DAYS PRIOR TO PROJECT CONSTRUCTION COMMENCEMENT.

TIMBER CONNECTIONS TO MEET NZS 3604 REQUIREMENTS

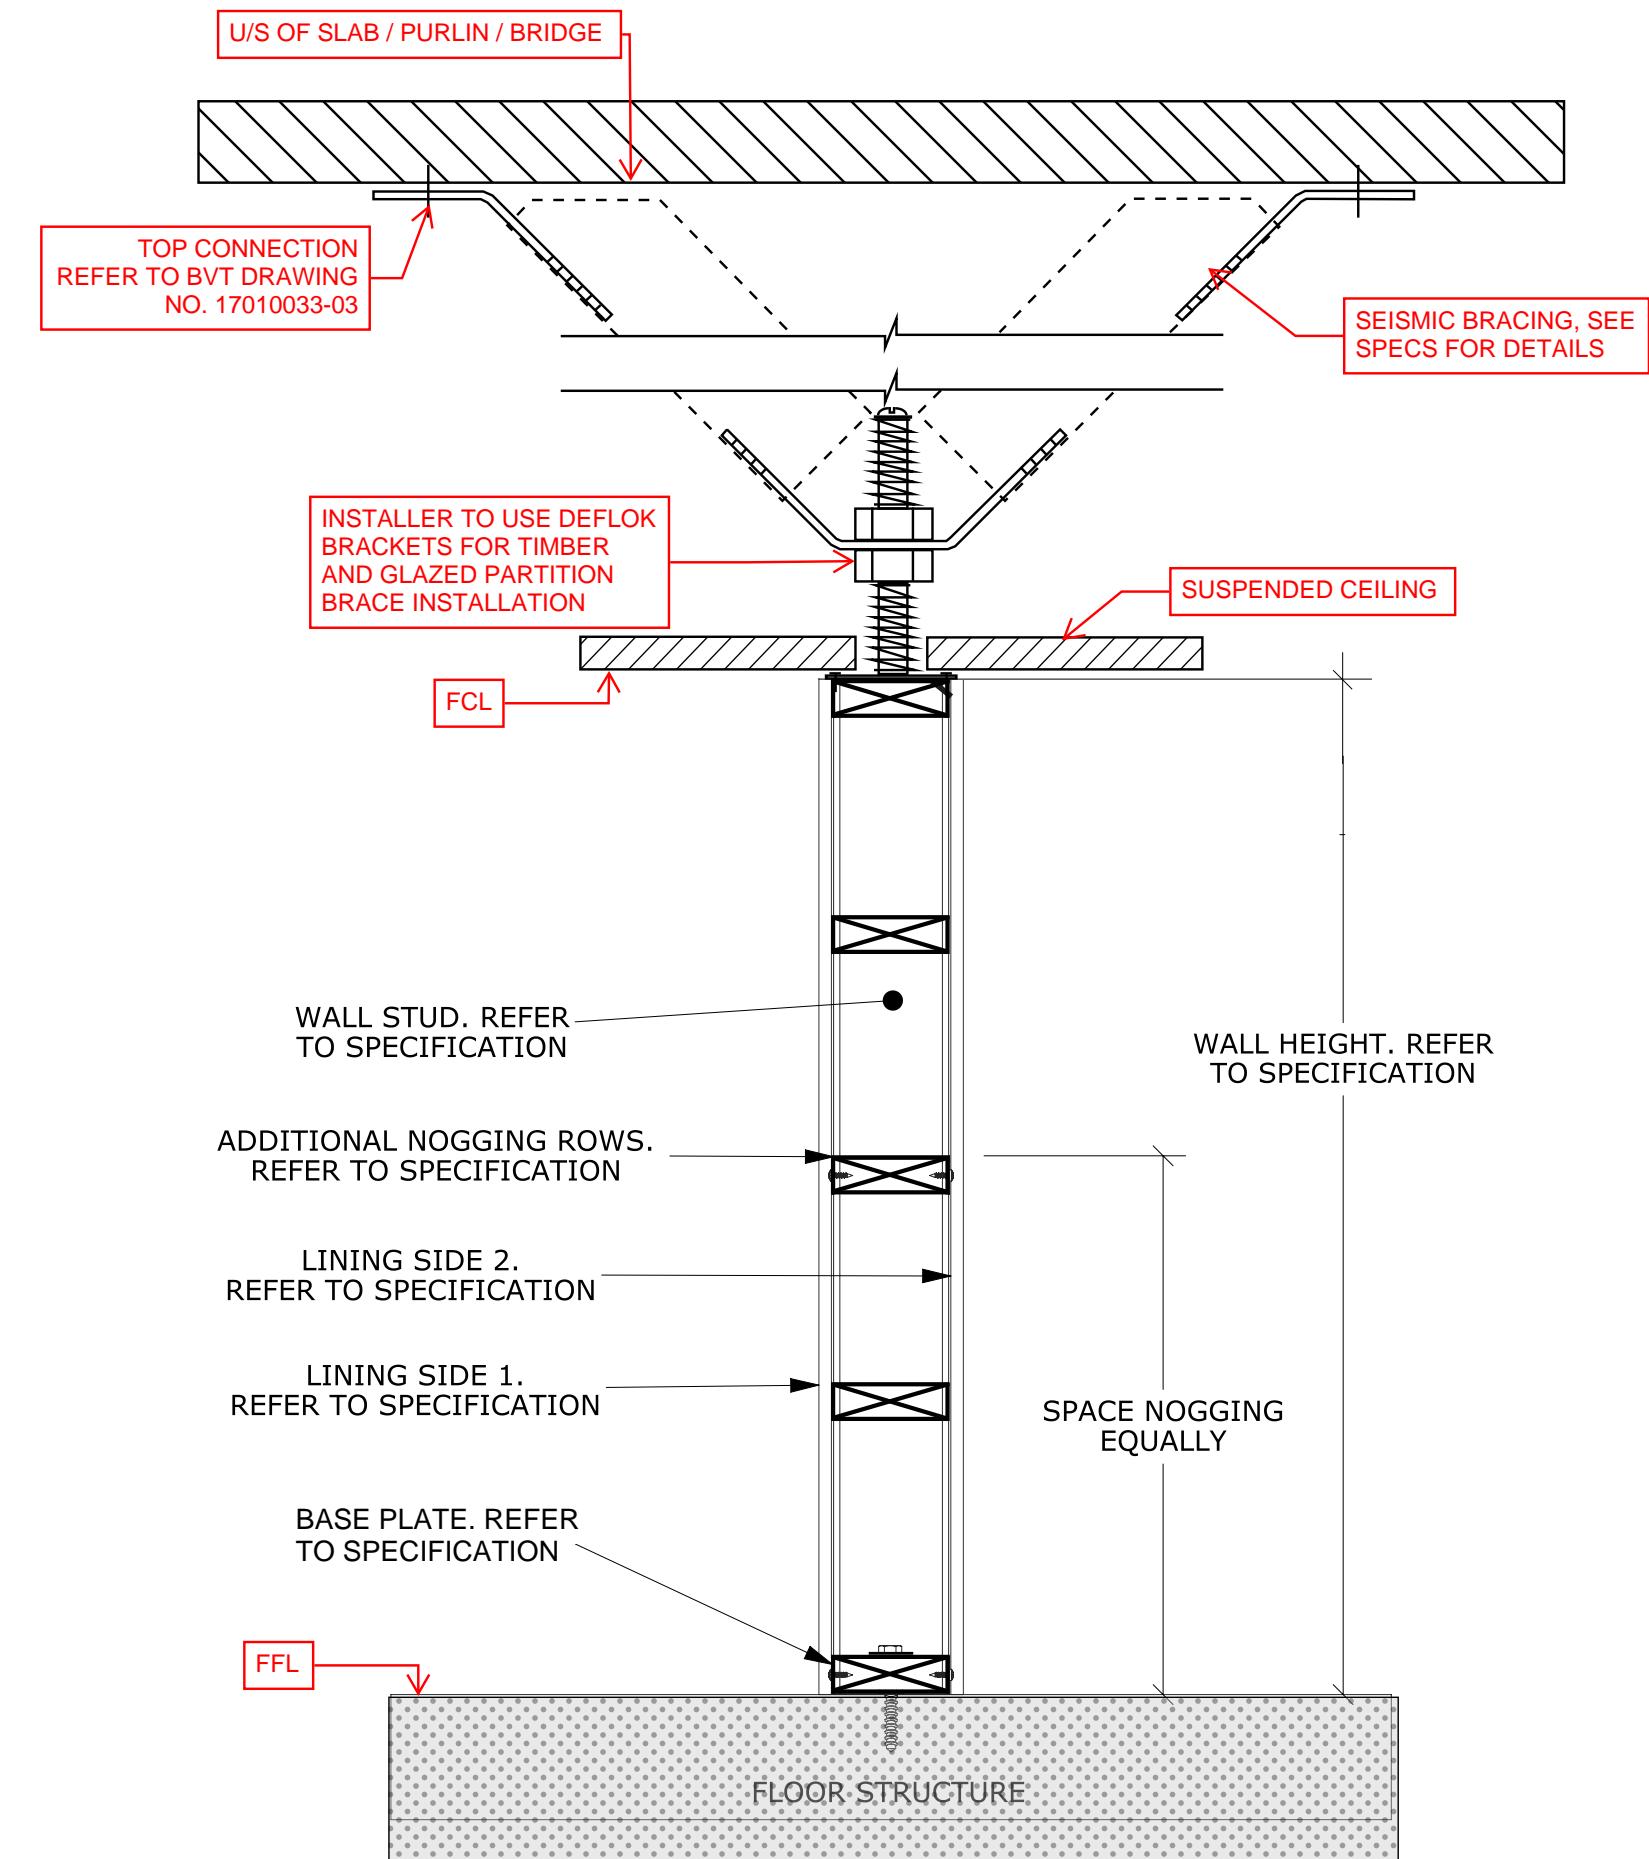

- NOTES:
1. REFER SPECIFICATION SHEET FOR CONTRACTOR AND INSTALLATION REQUIREMENTS
 2. ANY CHANGES ON SITE TO BE APPROVED BY BVT
 3. BRACE SPACING FOR PARTITION TYPE G02 TO BE MAX. 1200mm
 4. INSTALLER TO USE DEFLOK BRACKETS FOR BRACE INSTALLATION

DESIGNER:

Brevity

Victoria Park Market,
Unit 72B,
210 Victoria Street West
Auckland 1010

+64 9 216 7104
www.teambrevity.com

Tolerances (unless specified)	1-100	<1000	>1000
	± 2	± 10	± 70



Rev	Description
A	FOR CONSENT

Designed	BREVITY LTD	16/01/23
Drawn	BREVITY LTD	16/01/23
Approved	BREVITY LTD	16/01/23

SEISMIC BRACING LAYOUT -
TIMBER FRAME
PARTIAL HEIGHT PARTITION
UP TO CEILING HEIGHT

Scale
Do not Scale

DRG No. P057-11B SHEET 1 of 1